
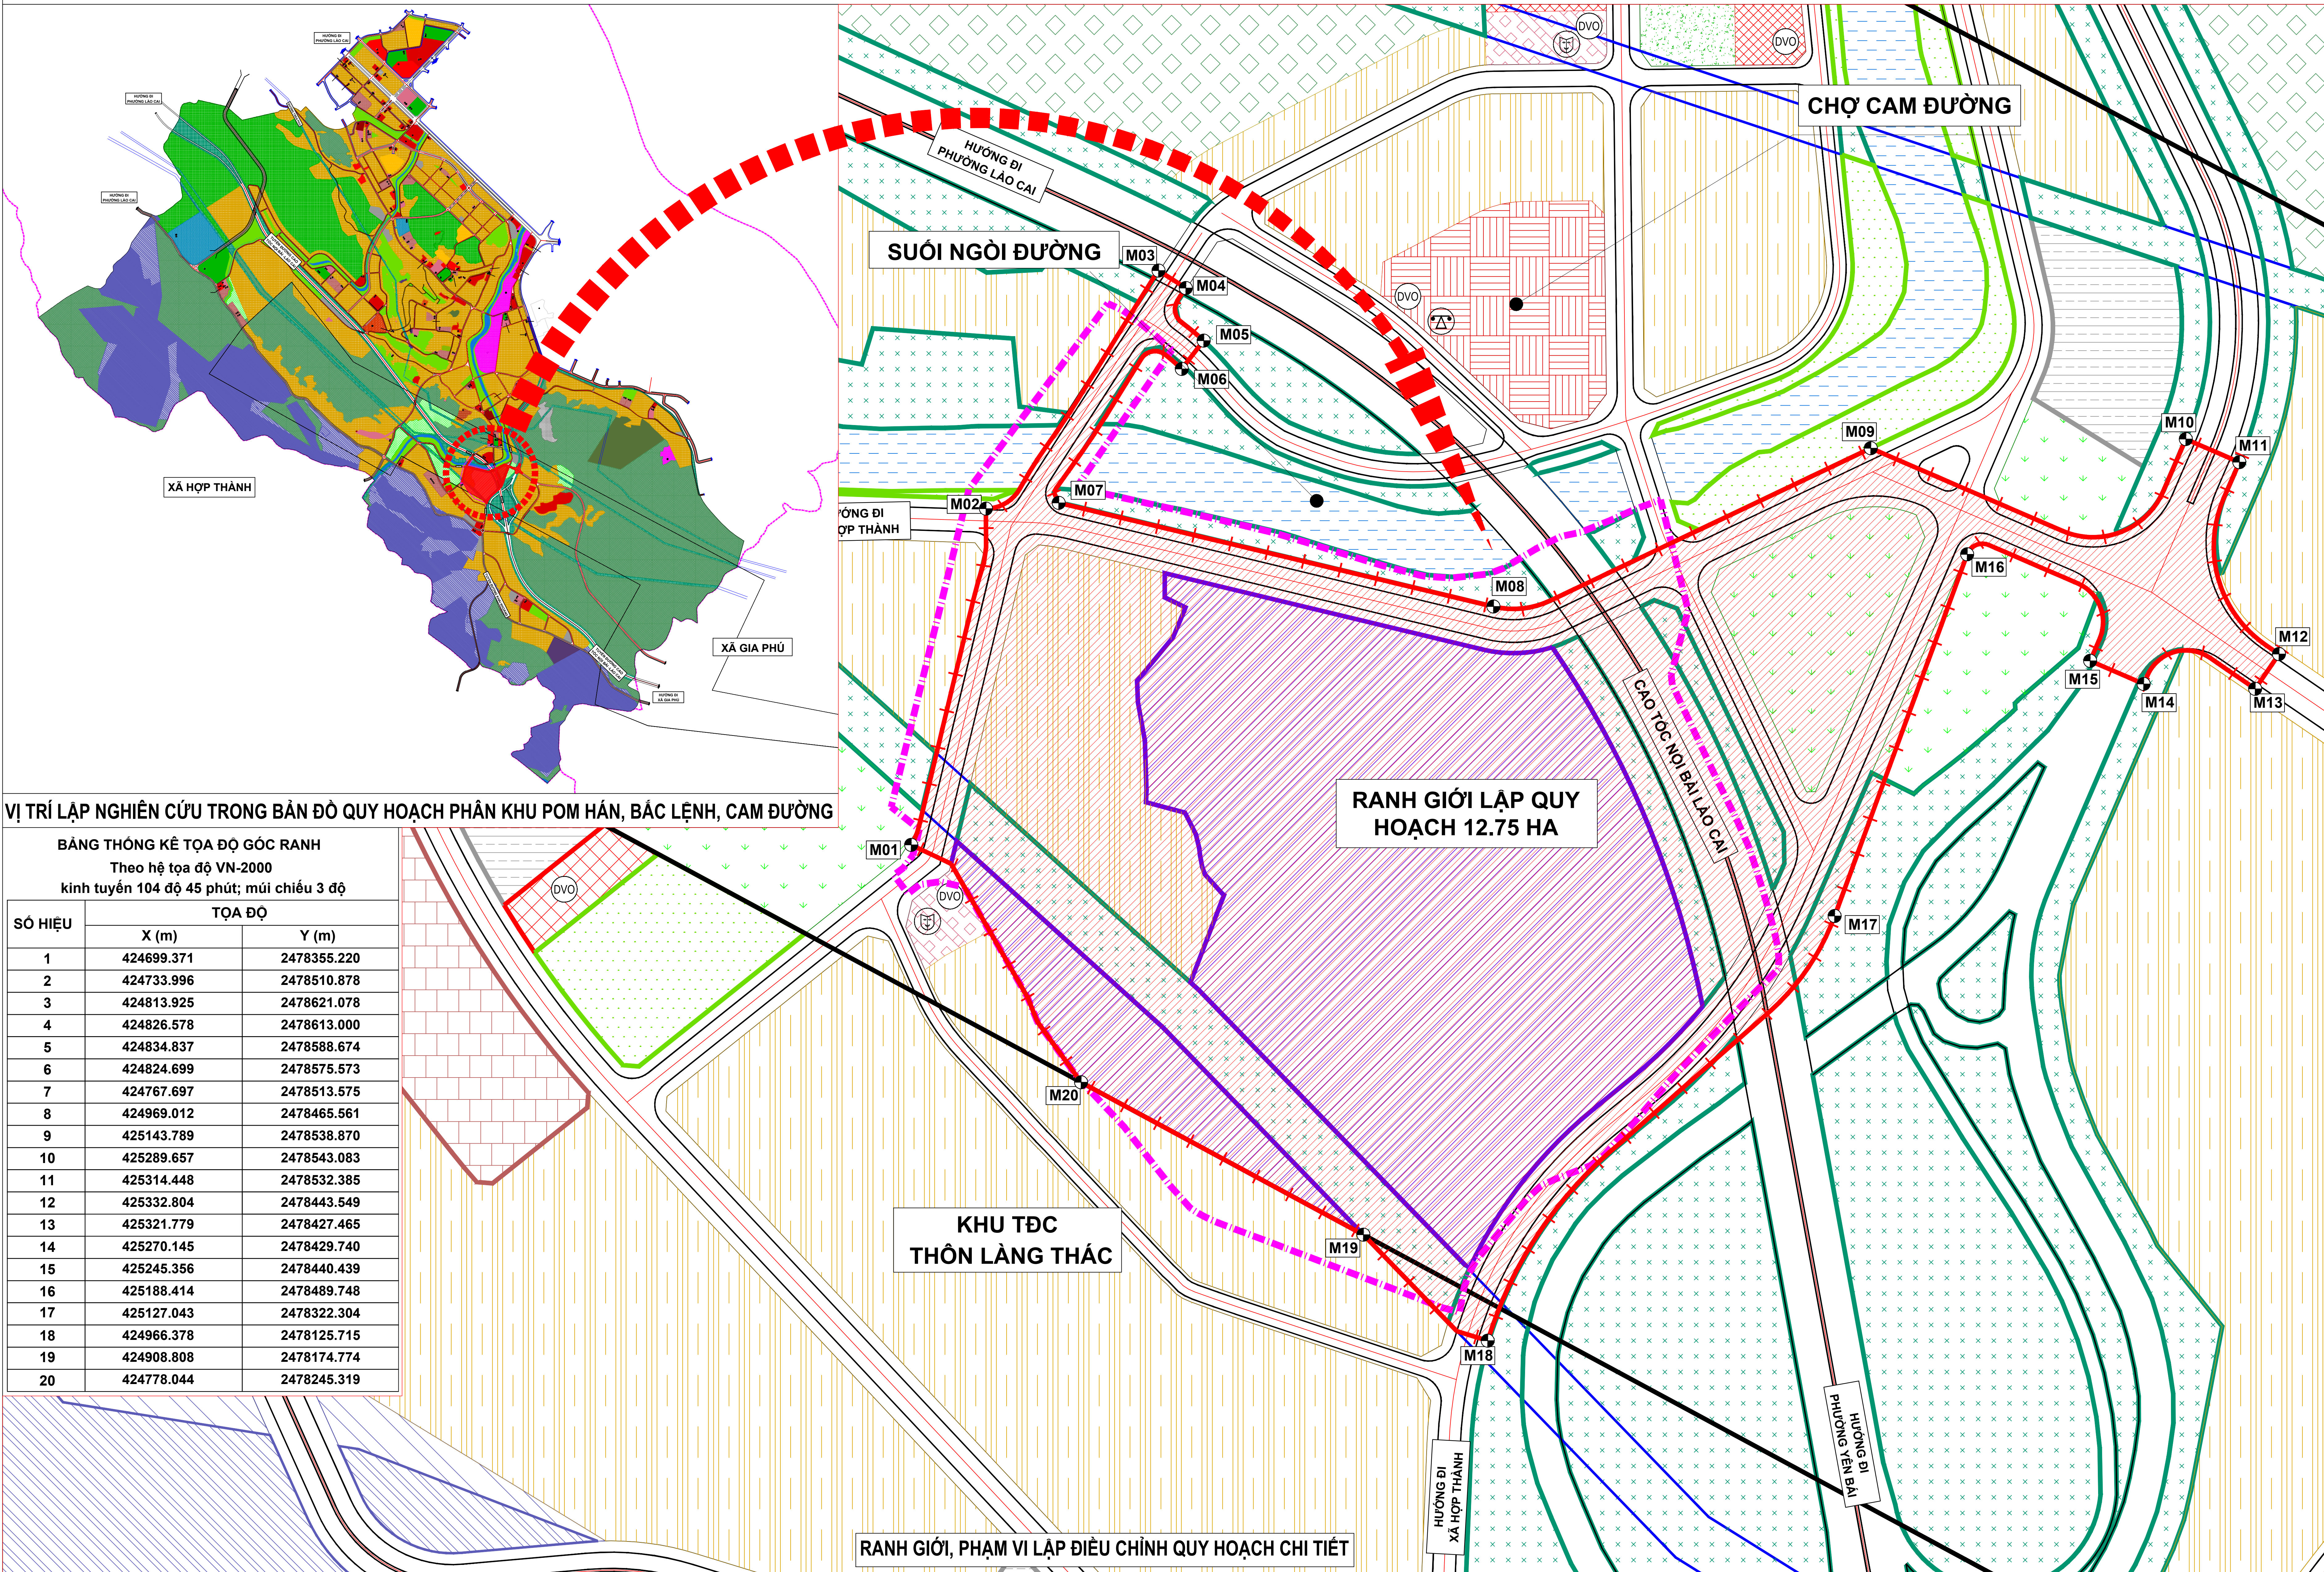


QUY HOẠCH CHI TIẾT CỤM CÔNG NGHIỆP CAM ĐƯỜNG 2 VÀ KHU DÂN CƯ THÔN THÁC,
PHƯỜNG CAM ĐƯỜNG, TỈNH LÀO CAI

ĐỊA ĐIỂM: PHƯỜNG CAM ĐƯỜNG, TỈNH LÀO CAI

QH-02: BẢN ĐỒ RANH GIỚI PHẠM VI LẬP QUY HOẠCH CHI TIẾT

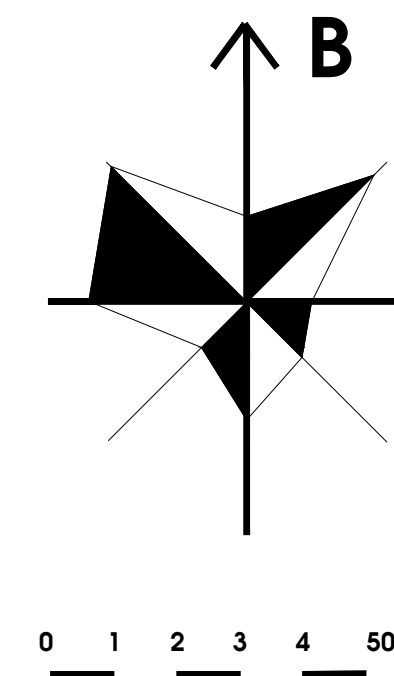

VỊ TRÍ LẬP NGHIÊN CỨU TRONG BẢN ĐỒ QUY HOẠCH PHÂN KHU POM HÁN, BẮC LỆNH, CAM ĐƯỜNG

BẢNG THÔNG KÊ TỌA ĐỘ GÓC RANH
Theo hệ tọa độ VN-2000
Kinh tuyến 104 độ 45 phút; múi chiều 3 độ

SỐ HIỆU	TỌA ĐỘ	
	X (m)	Y (m)
1	424699.371	2478355.220
2	424733.996	2478510.878
3	424813.925	2478621.078
4	424826.578	2478613.000
5	424834.837	2478588.674
6	424824.699	2478575.573
7	424767.697	2478513.575
8	424969.012	2478465.561
9	425143.789	2478538.870
10	425289.657	2478543.083
11	425314.448	2478532.385
12	425332.804	2478443.549
13	425321.779	2478427.465
14	425270.145	2478429.740
15	425245.356	2478440.439
16	425188.414	2478489.748
17	425127.043	2478322.304
18	424966.378	2478125.715
19	424908.808	2478174.774
20	424778.044	2478245.319

- 1. ĐIỀU CHỈNH TÊN QUY HOẠCH:**
 - TÊN QUY HOẠCH ĐÃ ĐƯỢC PHÊ DUYỆT: "QUY HOẠCH CHI TIẾT XÂY DỰNG TỶ LỆ 1/500 KHU DÂN CƯ THÔN LÀNG THÁC, XÃ CAM ĐƯỜNG, THÀNH PHỐ LÀO CAI"
 - ĐIỀU CHỈNH TÊN QUY HOẠCH: "CỤM CÔNG NGHIỆP CAM ĐƯỜNG 2, PHƯỜNG CAM ĐƯỜNG, TỈNH LÀO CAI"
- 2. VỊ TRÍ, PHẠM VI RANH GIỚI:**
 - KHU VỰC QUY HOẠCH THUỘC ĐỊA GIỚI PHƯỜNG CAM ĐƯỜNG, TỈNH LÀO CAI. RANH GIỚI KHU VỰC QUY HOẠCH ĐƯỢC XÁC ĐỊNH NHƯ SAU:
 - + PHÍA BẮC GIÁP SÚOI NGÔI ĐƯỜNG;
 - + PHÍA NAM GIÁP KHU DÂN CƯ;
 - + PHÍA ĐÔNG GIÁP ĐƯỜNG CAO TỐC NỘI BÀI - LÀO CAI;
 - + PHÍA TÂY GIÁP KHU TÁI ĐỊNH CƯ THÔN LÀNG THÁC.
- 3. QUY MÔ LẬP ĐIỀU CHỈNH QUY HOẠCH**
 - DIỆN TÍCH QUY HOẠCH ĐÃ ĐƯỢC PHÊ DUYỆT: 11,0HA
 - DIỆN TÍCH LẬP ĐIỀU CHỈNH QUY HOẠCH: 12,75HA
 - QUY HOẠCH ĐƯỢC LẬP TỶ LỆ BẢN ĐỒ 1/500.
- 4. TÍNH CHẤT KHU VỰC LẬP QUY HOẠCH:**

LÀ KHU CHỨC NĂNG TRONG TỔNG THỂ ĐÔ THỊ PHƯỜNG CAM ĐƯỜNG, ĐƯỢC XÁC ĐỊNH LÀ KHU SẢN XUẤT TIỂU THỦ CÔNG NGHIỆP; CÓ CHỨC NĂNG BỐ TRÍ TẬP TRUNG CÁC CƠ SỞ SẢN XUẤT ĐANG HOẠT ĐỘNG TRONG KHU DÂN CƯ VÀ CÁC CƠ SỞ CƠ NHU CẦU ĐẦU TƯ XÂY DỰNG MỚI; THỰC HIỆN VIỆC DI DỜI, SẮP XẾP, MỞ RỘNG HOẶC PHÁT TRIỂN SẢN XUẤT THEO QUY HOẠCH ĐƯỢC PHÊ DUYỆT, ĐỒNG THỜI BẢO ĐẢM SỰ ĐỒNG BỘ VỀ HẠ TẦNG XÃ HỘI VÀ HẠ TẦNG KỸ THUẬT TRÊN ĐỊA BÀN ĐÔ THỊ PHƯỜNG CAM ĐƯỜNG.
- 5. MỤC TIÊU**

VIỆC XÂY DỰNG KHU SẢN XUẤT CÔNG NGHIỆP NHẪM TẠO LẬP CƠ SỞ PHÁP LÝ ĐỂ THỰC HIỆN ĐẦU TƯ XÂY DỰNG HỆ THỐNG HẠ TẦNG KỸ THUẬT; THU HÚT, VẬN ĐỘNG CÁC CƠ SỞ SẢN XUẤT ĐANG HOẠT ĐỘNG TRONG KHU DÂN CƯ VÀ CÁC CƠ SỞ CƠ NHU CẦU ĐẦU TƯ XÂY DỰNG MỚI, DI DỜI, SẮP XẾP HOẶC MỞ RỘNG, PHÁT TRIỂN SẢN XUẤT THEO QUY HOẠCH ĐƯỢC PHÊ DUYỆT; QUA ĐÓ GÓP PHẦN THÚC ĐẨY CHUYỂN DỊCH CƠ CẤU KINH TẾ, TĂNG CƯỜNG HIỆU LỰC, HIỆU QUẢ QUẢN LÝ, SỬ DỤNG ĐẤT ĐAI VÀ BẢO ĐẢM TRẬT TỰ XÂY DỰNG THEO QUY ĐỊNH CỦA PHÁP LUẬT. ĐỒNG THỜI LÀM CĂN CỨ CHO CÁC BƯỚC TRIỂN KHAI TIẾP THEO.

KÝ HIỆU:	
	RANH KHU VỰC LẬP QUY HOẠCH
	RANH GIỚI QUY HOẠCH ĐÃ ĐƯỢC PHÊ DUYỆT

HIỆN TRẠNG	QUY HOẠCH
	ĐẤT NHÓM NHÀ Ở
	ĐẤT HỖN HỢP NHÓM NHÀ Ở VÀ DỊCH VỤ
	ĐẤT VĂN HÓA
	ĐẤT CÔNG TRÌNH CÔNG CỘNG KHÁC
	ĐẤT THỂ DỤC THỂ THAO
	ĐẤT TRƯỜNG THPT
	ĐẤT TRƯỜNG THCS, TIỂU HỌC, MN
	TRƯỜNG LIÊN CẤP
	ĐẤT CÂY XANH SỬ DỤNG CÔNG CỘNG
	ĐẤT CÂY XANH SỬ DỤNG HẠN CHẾ
	ĐẤT CÂY XANH CHUYỂN DỤNG
	ĐẤT KHAI THÁC, CHẾ BIẾN KHOÁNG SẢN, SX VLXD
	ĐẤT CƠ SỞ SẢN XUẤT KHÁC
	ĐẤT KHU DỊCH VỤ
	ĐẤT DI TÍCH, TÔN GIÁO
	ĐẤT AN NINH
	ĐẤT QUỐC PHÒNG
	ĐẤT BÃI ĐỒ XE
	ĐẤT HẠ TẦNG KỸ THUẬT KHÁC
	ĐẤT RỪNG SẢN XUẤT
	ĐẤT SẢN XUẤT NÔNG NGHIỆP
	SÔNG, SUỐI, KÊNH, RẠCH